Master Facility Plan of Wiring.com

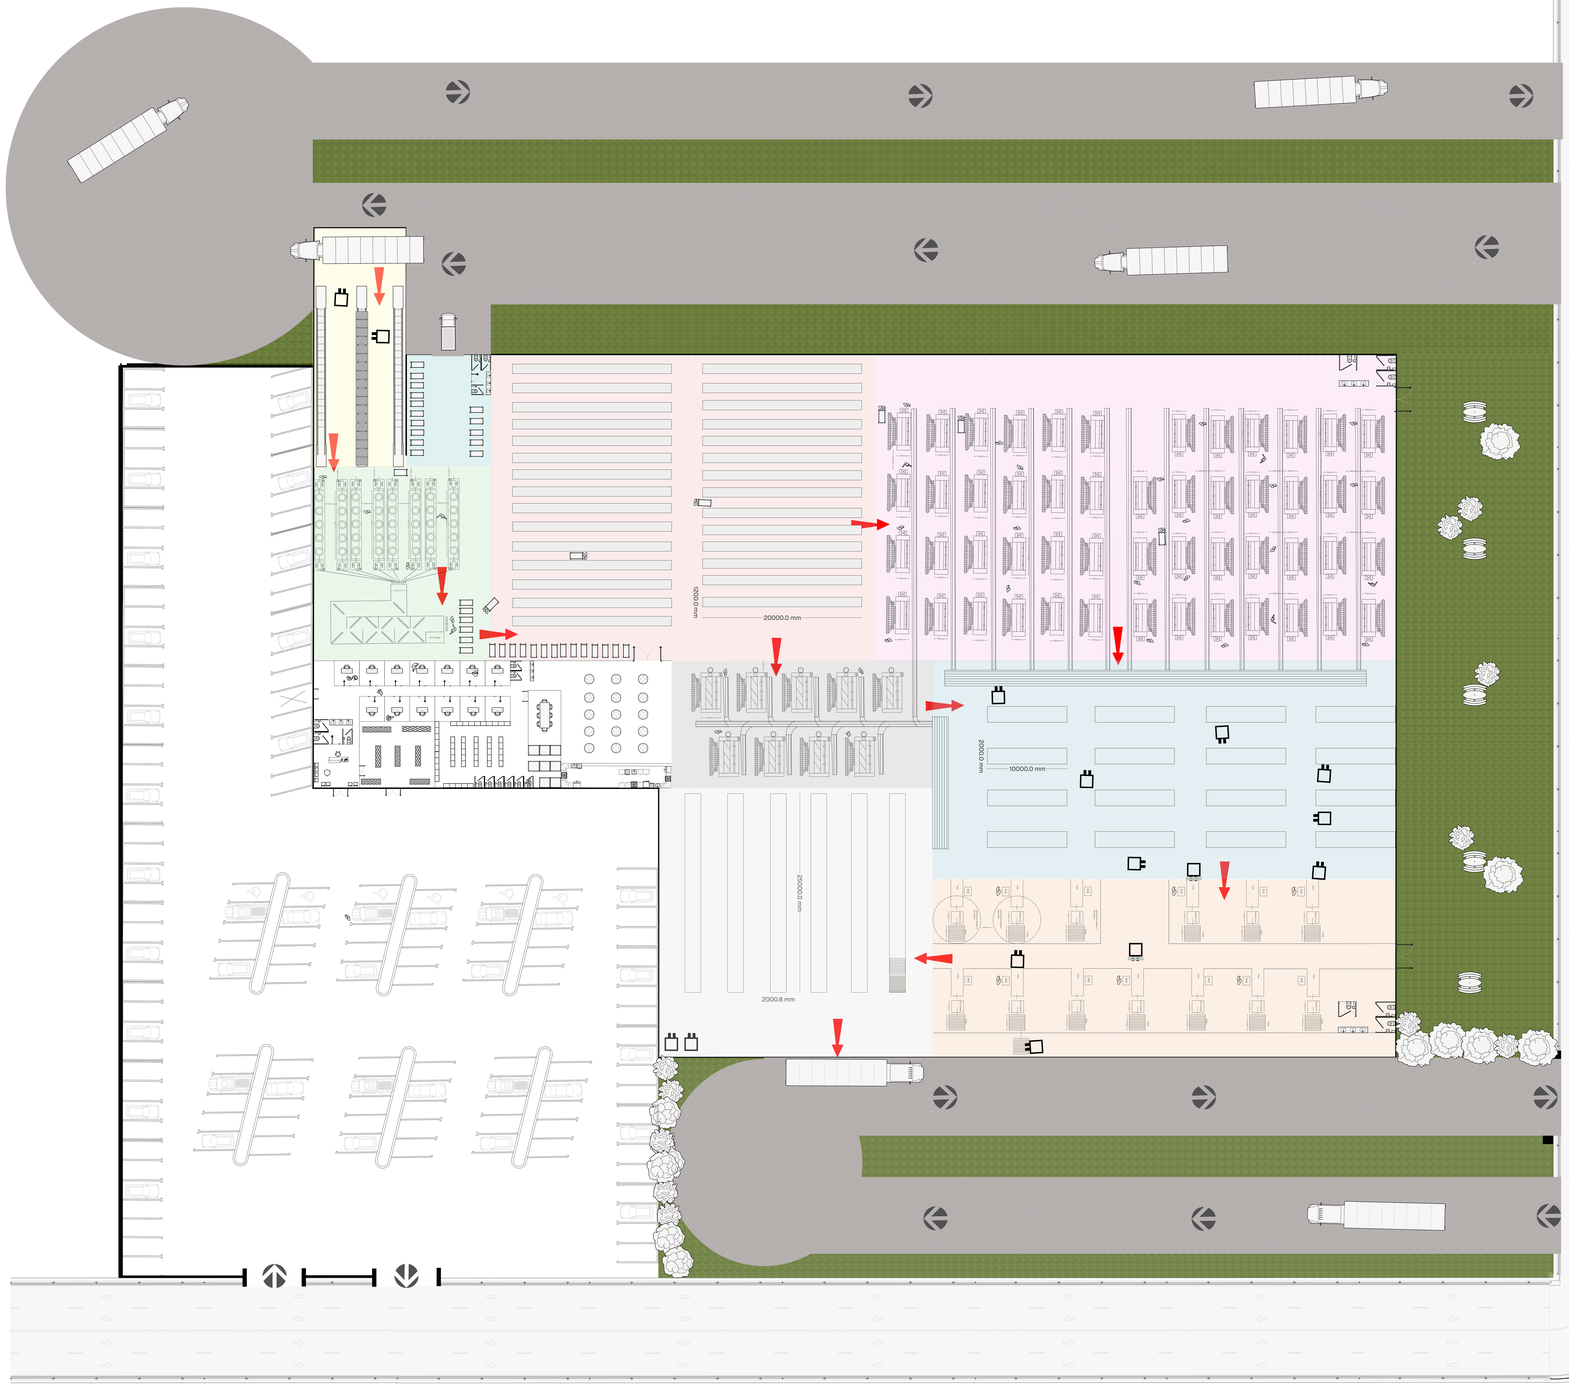

LEGEND:

- Truck
- KLP RollStop System
- Wire Drawing Machine
- Galvanizing Bath
- Double-sided Racks
- Low-lying Gravity Rollers
- Lockers
- Racks
- Hexagonal Machine
- Wire Welding Machine
- Robotic Arm & Pallet
- Trees
- Raw Steel Coil
- Picnic Table
- Forklift
- Bin with Wheels
- Shower

- Raw Material Storage
- Preparation Department
- Scrap Storage
- Prepared Wire Storage
- Hex Department
- Processed Wire Storage
- Packing Department
- Welding Department
- Amenities
- Finished Goods Storage

Scale 1:200

By Kaylee Meyer (41763939); John Faul (33743983); Helman Lekubo (33731934).